

K0+000 – K0+200 · Acceso, cuñas del anillo vial y glorieta

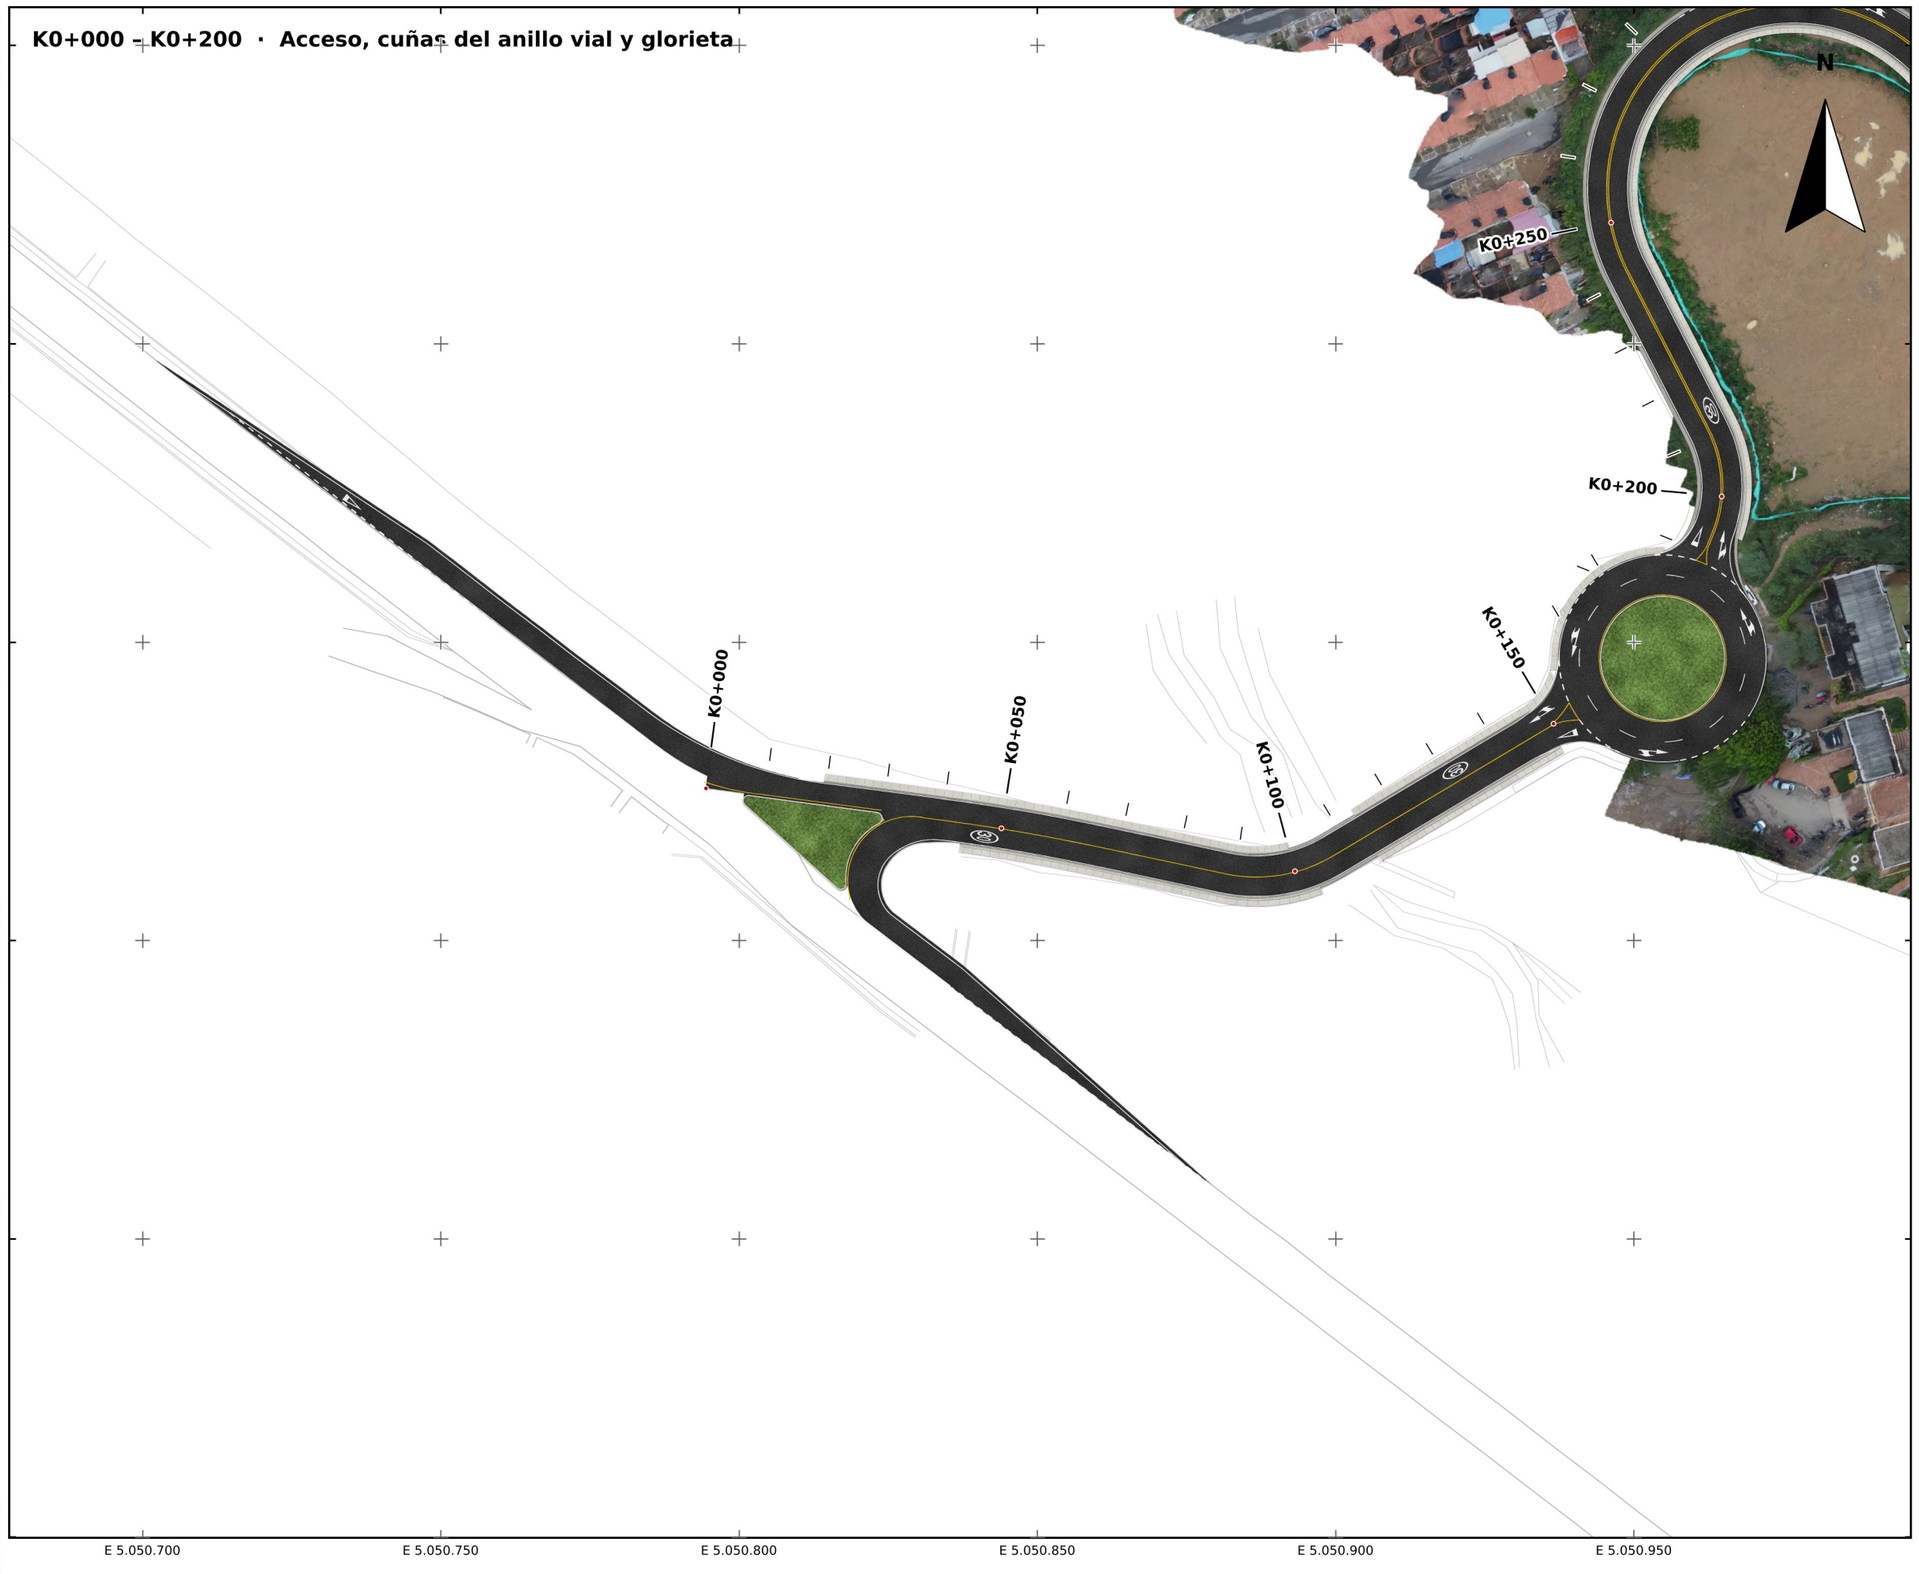

LOCALIZACIÓN DE LA LÁMINA

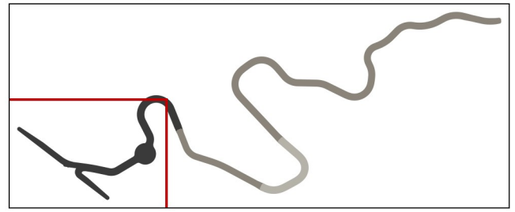

CONVENCIONES

- Pavimento flexible (MDC-19)
- Tratamiento superficial doble (TSD)
- Pavimento rígido MR-45 (losas 3,50 × 3,75 m)
- Losa irregular con malla 1/2" @ 0,30
- Cuneta en concreto
- Bordillo
- Andén en concreto (juntas c/1,50 m)
- Isleta (zona verde)
- Demarcación blanca
- Demarcación amarilla (eje)
- Defensa metálica
- Abscisa sobre el eje de diseño
- Levantamiento (fuera de ortofoto)

Fuente: CUCUTA_DG_PP_001-06_V2 y CUCUTA_DG_SEN_001-03_V2 (diseño V2); ortofoto 10 cm; levantamiento CAD-DG Las Delicias. Anchos tomados de las capas BV, Cuneta y ANDÉN con offset perpendicular al eje cada 0,50 m. Abscisas: eje 001 + eje 002 (ecuación K0+171,358 = K0+170,980).

ESCALA 1:1000

0 10 20 30 40 50 m

PLANTA REALISTA

DISEÑO GEOMÉTRICO V2

PROYECTO

Vía Belén – Las Delicias
Cúcuta, Norte de Santander

CONTENIDO

Planta realista – tramo K0+000 – K0+200
Acceso, cuñas del anillo vial y glorieta


SISTEMA

MAGNA-SIRGAS Origen Nacional
(CTM-12) · cotas en metros

ESCALA	LÁMINA
1:1000 · doble carta	**1 / 7**



LOCALIZACIÓN DE LA LÁMINA

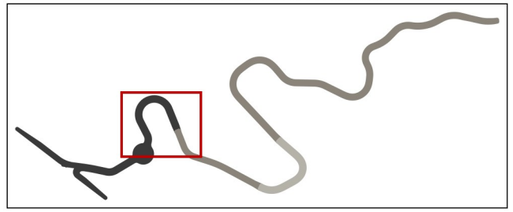

CONVENCIONES

- Pavimento flexible (MDC-19)
- Tratamiento superficial doble (TSD)
- Pavimento rígido MR-45 (losas 3,50 × 3,75 m)
- Losa irregular con malla 1/2" @ 0,30
- Cuneta en concreto
- Bordillo
- Andén en concreto (juntas c/1,50 m)
- Isleta (zona verde)
- Demarcación blanca
- Demarcación amarilla (eje)
- Defensa metálica
- Abscisa sobre el eje de diseño
- Levantamiento (fuera de ortofoto)

Fuente: CUCUTA_DG_PP_001-06_V2 y CUCUTA_DG_SEN_001-03_V2 (diseño V2); ortofoto 10 cm; levantamiento CAD-DG Las Delicias. Anchos tomados de las capas BV, Cuneta y ANDEN con offset perpendicular al eje cada 0,50 m. Abscisas: eje 001 + eje 002 (ecuación K0+171,358 = K0+170,980).

ESCALA 1:500

0 5 10 15 20 25 m

PLANTA REALISTA

DISEÑO GEOMÉTRICO V2

PROYECTO

Vía Belén – Las Delicias
Cúcuta, Norte de Santander

CONTENIDO

Planta realista – tramo K0+180 – K0+420
Eje 002 – pavimento flexible


SISTEMA

MAGNA-SIRGAS Origen Nacional
(CTM-12) · cotas en metros

ESCALA	LÁMINA
1:500 · doble carta	**2 / 7**



LOCALIZACIÓN DE LA LÁMINA

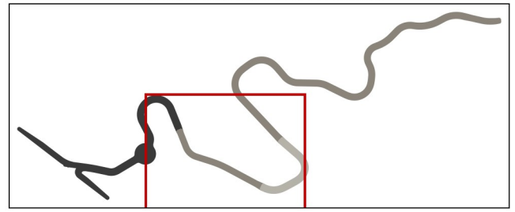

CONVENCIONES

- Pavimento flexible (MDC-19)
- Tratamiento superficial doble (TSD)
- Pavimento rígido MR-45 (losas 3,50 × 3,75 m)
- Losa irregular con malla 1/2" @ 0,30
- Cuneta en concreto
- Bordillo
- Andén en concreto (juntas c/1,50 m)
- Isleta (zona verde)
- Demarcación blanca
- Demarcación amarilla (eje)
- Defensa metálica
- Abscisa sobre el eje de diseño
- Levantamiento (fuera de ortofoto)

Fuente: CUCUTA_DG_PP_001-06_V2 y CUCUTA_DG_SEN_001-03_V2 (diseño V2); ortofoto 10 cm; levantamiento CAD-DG Las Delicias. Anchos tomados de las capas BV, Cuneta y ANDEN con offset perpendicular al eje cada 0,50 m. Abscisas: eje 001 + eje 002 (ecuación K0+171,358 = K0+170,980).

ESCALA 1:1000

0 10 20 30 40 50 m

PLANTA REALISTA

DISEÑO GEOMÉTRICO V2

PROYECTO

Vía Belén – Las Delicias
Cúcuta, Norte de Santander

CONTENIDO

Planta realista – tramo K0+380 – K0+620
Transición flexible – TSD (5,00 m)


SISTEMA

MAGNA-SIRGAS Origen Nacional
(CTM-12) · cotas en metros

ESCALA	LÁMINA
1:1000 · doble carta	**3 / 7**



LOCALIZACIÓN DE LA LÁMINA

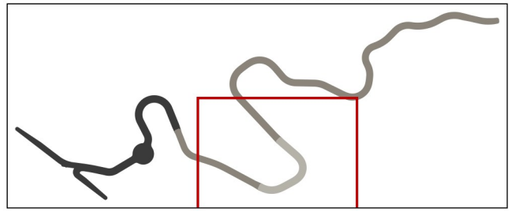

CONVENCIONES

- Pavimento flexible (MDC-19)
- Tratamiento superficial doble (TSD)
- Pavimento rígido MR-45 (losas 3,50 × 3,75 m)
- Losa irregular con malla 1/2" @ 0,30
- Cuneta en concreto
- Bordillo
- Andén en concreto (juntas c/1,50 m)
- Isleta (zona verde)
- Demarcación blanca
- Demarcación amarilla (eje)
- Defensa metálica
- Abscisa sobre el eje de diseño
- Levantamiento (fuera de ortofoto)

Fuente: CUCUTA_DG_PP_001-06_V2 y CUCUTA_DG_SEN_001-03_V2 (diseño V2); ortofoto 10 cm; levantamiento CAD-DG Las Delicias. Anchos tomados de las capas BV, Cuneta y ANDEN con offset perpendicular al eje cada 0,50 m. Abscisas: eje 001 + eje 002 (ecuación K0+171,358 = K0+170,980).

ESCALA 1:1000

0 10 20 30 40 50 m

PLANTA REALISTA

DISEÑO GEOMÉTRICO V2

PROYECTO

Vía Belén – Las Delicias
Cúcuta, Norte de Santander

CONTENIDO

Planta realista – tramo K0+580 – K0+800
Pavimento rígido – despiece de losas

SISTEMA


MAGNA-SIRGAS Origen Nacional
(CTM-12) · cotas en metros

ESCALA	LÁMINA
1:1000 · doble carta	**4 / 7**

K0+780 – K1+120 ▫ TSD 6,00 m con cuneta



LOCALIZACIÓN DE LA LÁMINA

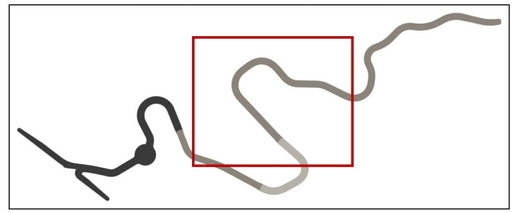

CONVENCIONES

- Pavimento flexible (MDC-19)
- Tratamiento superficial doble (TSD)
- Pavimento rígido MR-45 (losas 3,50 × 3,75 m)
- Losa irregular con malla 1/2" @ 0,30
- Cuneta en concreto
- Bordillo
- Andén en concreto (juntas c/1,50 m)
- Isleta (zona verde)
- Demarcación blanca
- Demarcación amarilla (eje)
- Defensa metálica
- Abscisa sobre el eje de diseño
- Levantamiento (fuera de ortofoto)

Fuente: CUCUTA_DG_PP_001-06_V2 y CUCUTA_DG_SEN_001-03_V2 (diseño V2); ortofoto 10 cm; levantamiento CAD-DG Las Delicias. Anchos tomados de las capas BV, Cuneta y ANDÉN con offset perpendicular al eje cada 0,50 m. Abscisas: eje 001 + eje 002 (ecuación K0+171,358 = K0+170,980).

ESCALA 1:1000

0 10 20 30 40 50 m

PLANTA REALISTA

DISEÑO GEOMÉTRICO V2

PROYECTO

Vía Belén – Las Delicias
Cúcuta, Norte de Santander

CONTENIDO


Planta realista – tramo K0+780 – K1+120
TSD 6,00 m con cunetas

SISTEMA


MAGNA-SIRGAS Origen Nacional
(CTM-12) · cotas en metros

ESCALA	LÁMINA
1:1000 · doble carta	**5 / 7**

K1+100 – K1+400 · TSD 6,00 m con cuetas

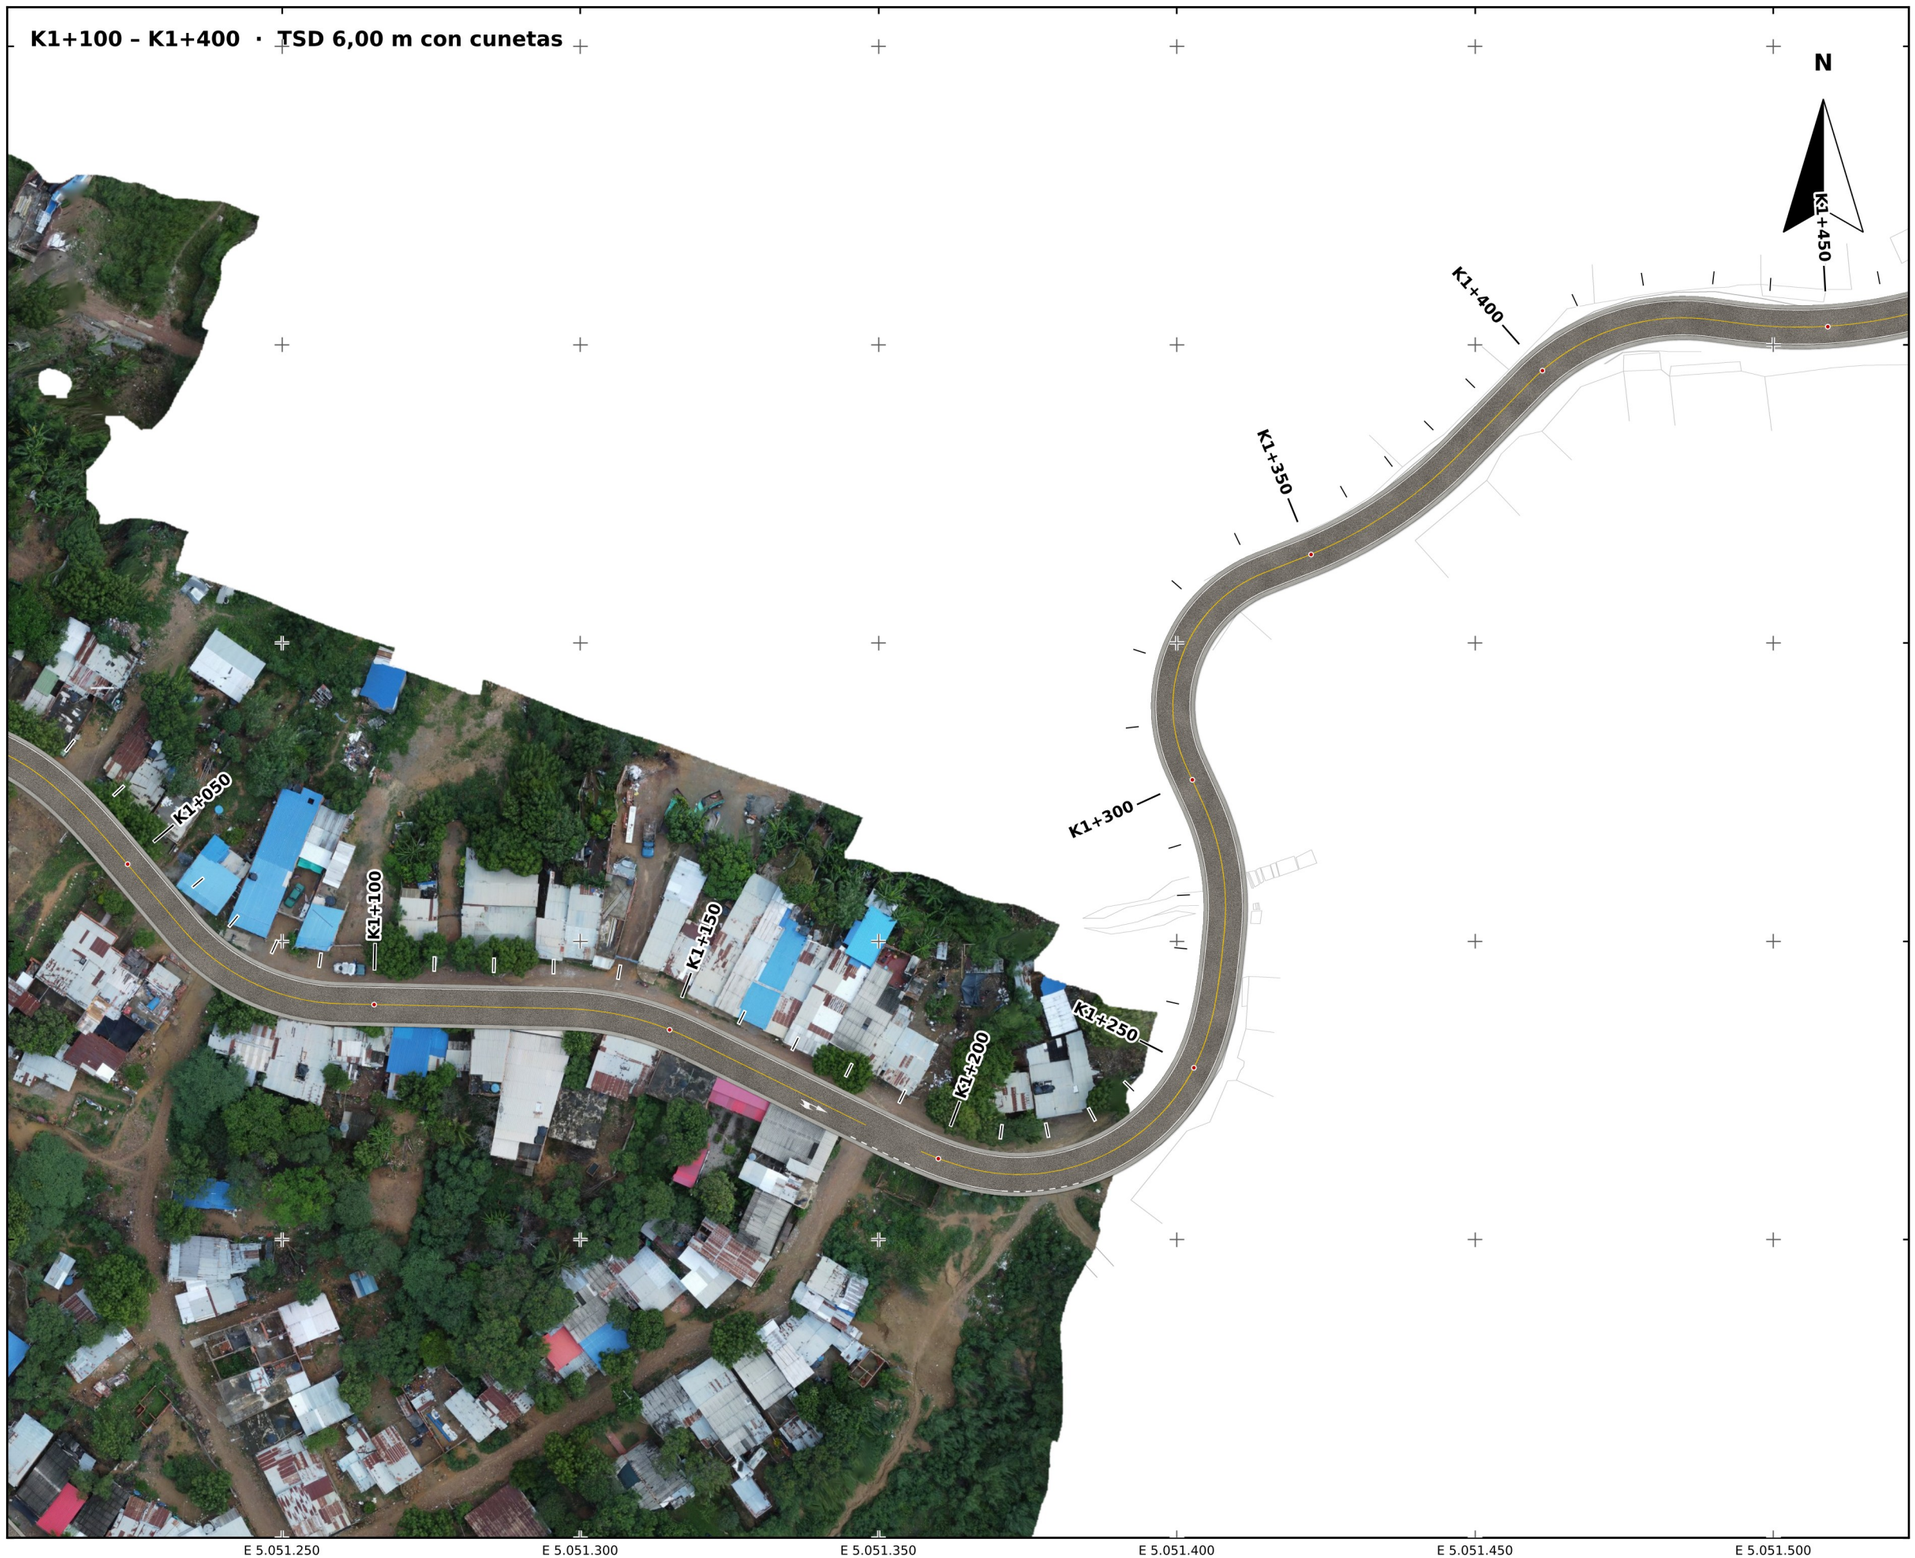

LOCALIZACIÓN DE LA LÁMINA

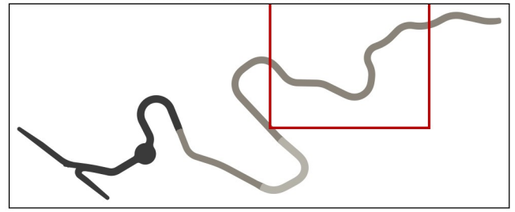

CONVENCIONES

- Pavimento flexible (MDC-19)
- Tratamiento superficial doble (TSD)
- Pavimento rígido MR-45 (losas 3,50 × 3,75 m)
- Losa irregular con malla 1/2" @ 0,30
- Cuneta en concreto
- Bordillo
- Andén en concreto (juntas c/1,50 m)
- Isleta (zona verde)
- Demarcación blanca
- Demarcación amarilla (eje)
- Defensa metálica
- Abscisa sobre el eje de diseño
- Levantamiento (fuera de ortofoto)

Fuente: CUCUTA_DG_PP_001-06_V2 y CUCUTA_DG_SEN_001-03_V2 (diseño V2); ortofoto 10 cm; levantamiento CAD-DG Las Delicias. Anchos tomados de las capas BV, Cuneta y ANDÉN con offset perpendicular al eje cada 0,50 m. Abscisas: eje 001 + eje 002 (ecuación K0+171,358 = K0+170,980).

ESCALA 1:1000

0 10 20 30 40 50 m

PLANTA REALISTA

DISEÑO GEOMÉTRICO V2

PROYECTO

Vía Belén – Las Delicias
Cúcuta, Norte de Santander

CONTENIDO


Planta realista – tramo K1+100 – K1+400
TSD 6,00 m con cunetas

SISTEMA


MAGNA-SIRGAS Origen Nacional
(CTM-12) · cotas en metros

ESCALA	LÁMINA
1:1000 · doble carta	**6 / 7**

K1+380 – K1+609 · TSD 6,00 m / 5,00 m – tramo final

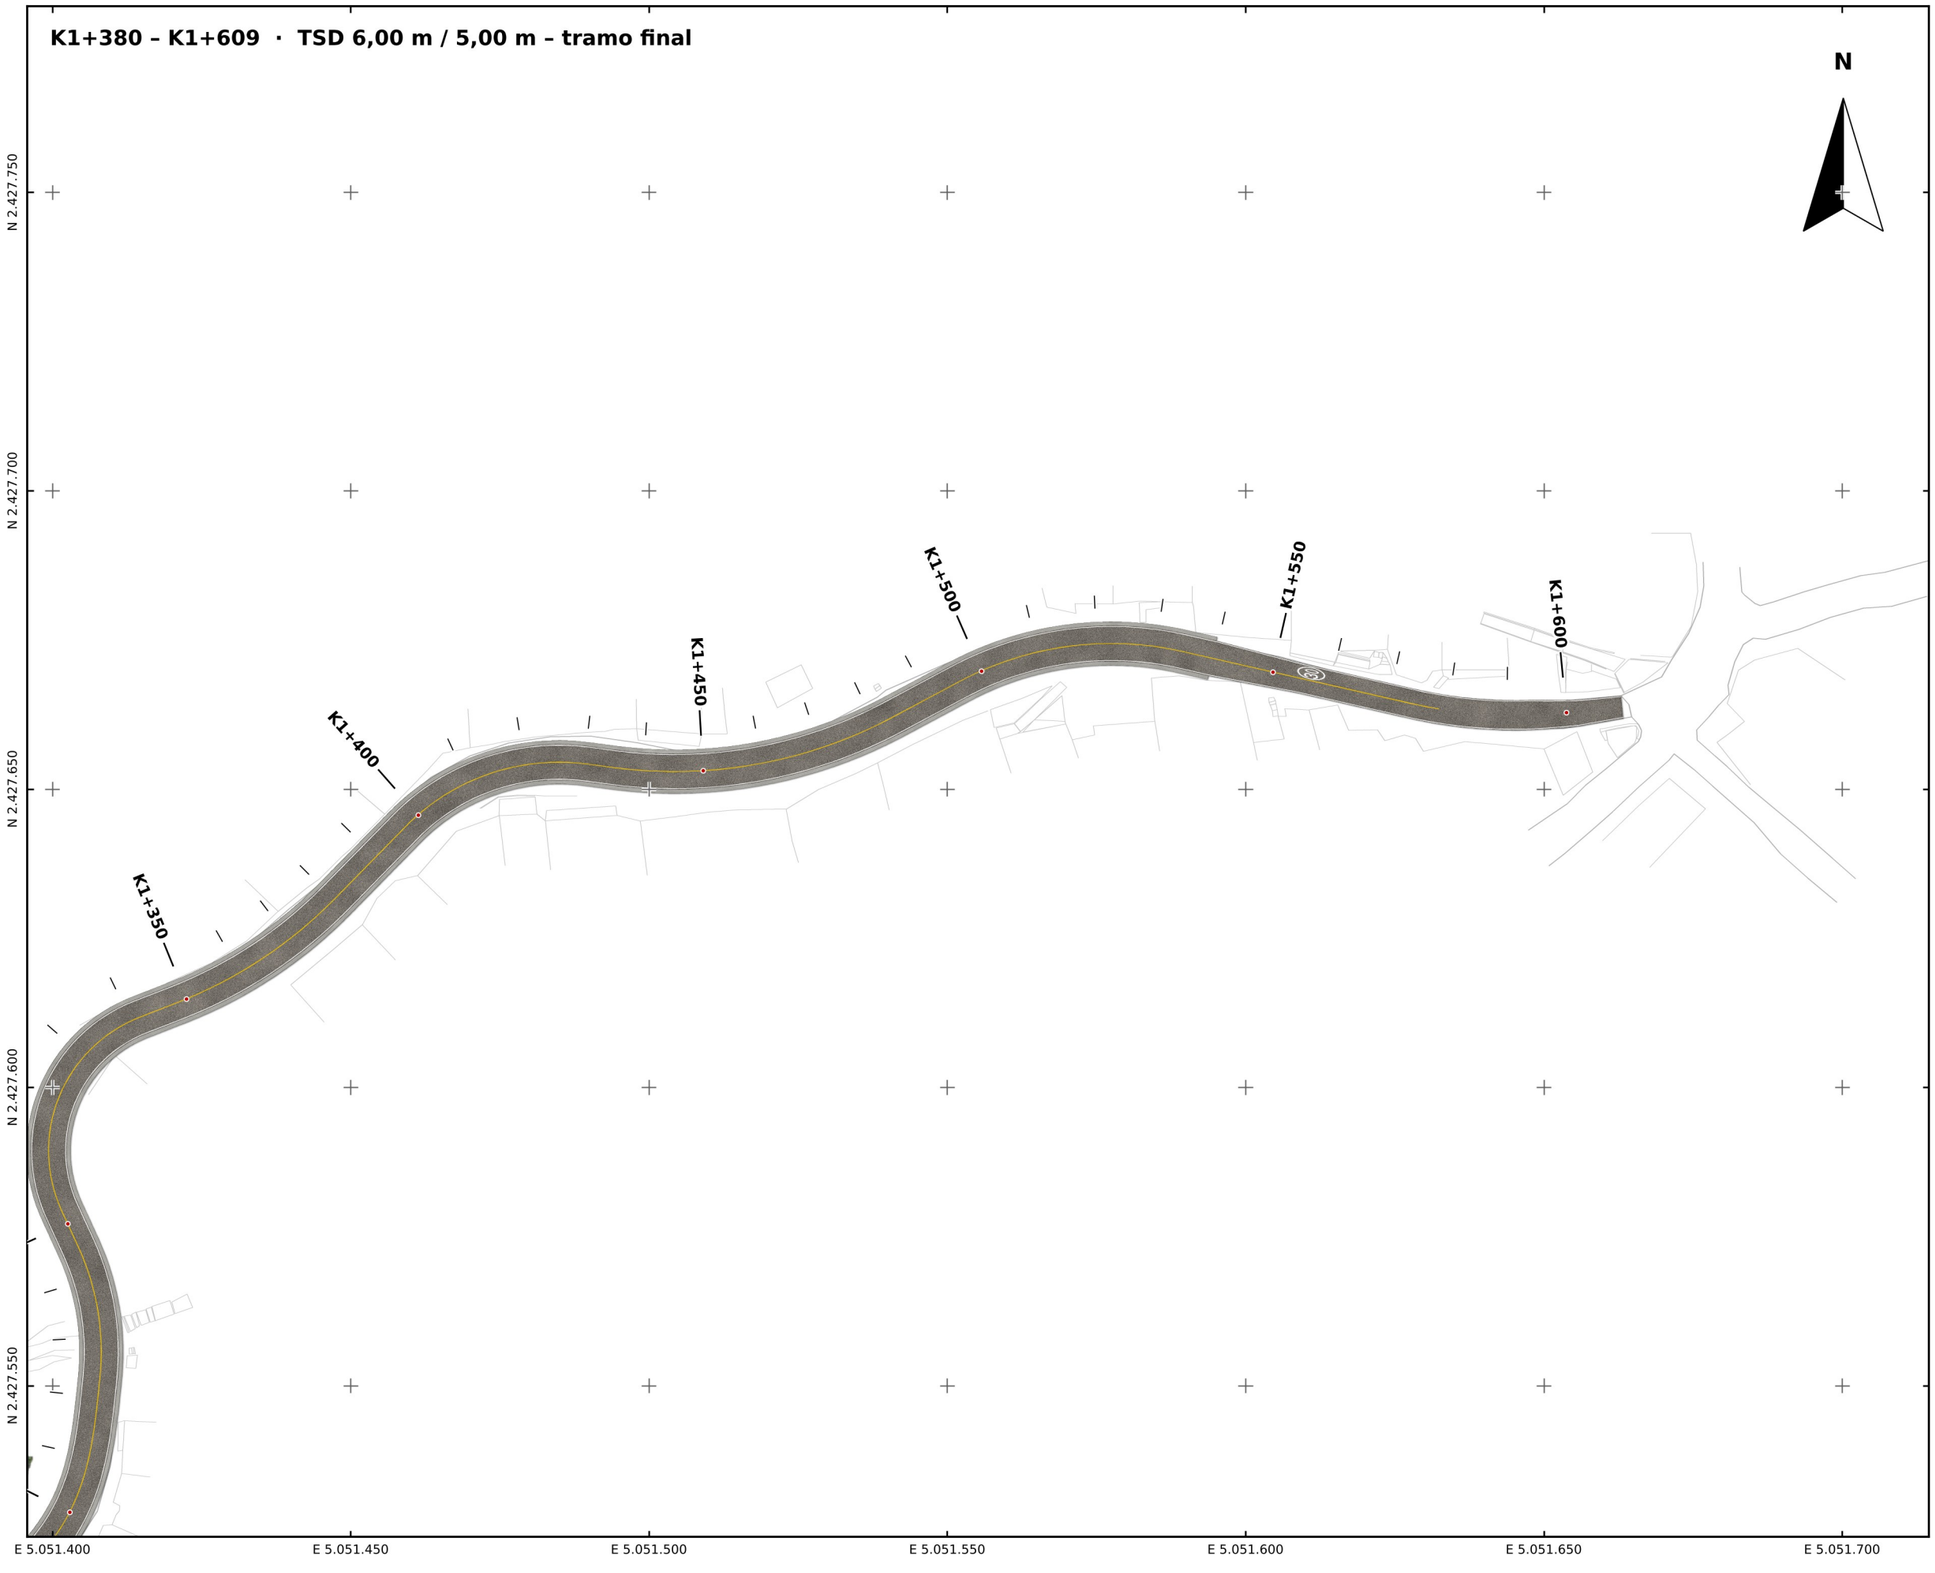

LOCALIZACIÓN DE LA LÁMINA

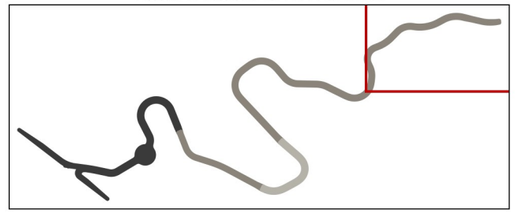

CONVENCIONES

- Pavimento flexible (MDC-19)
- Tratamiento superficial doble (TSD)
- Pavimento rígido MR-45 (losas 3,50 × 3,75 m)
- Losa irregular con malla 1/2" @ 0,30
- Cuneta en concreto
- Bordillo
- Andén en concreto (juntas c/1,50 m)
- Isleta (zona verde)
- Demarcación blanca
- Demarcación amarilla (eje)
- Defensa metálica
- Abscisa sobre el eje de diseño
- Levantamiento (fuera de ortofoto)

Fuente: CUCUTA_DG_PP_001-06_V2 y CUCUTA_DG_SEN_001-03_V2 (diseño V2); ortofoto 10 cm; levantamiento CAD-DG Las Delicias. Anchos tomados de las capas BV, Cuneta y ANDÉN con offset perpendicular al eje cada 0,50 m. Abscisas: eje 001 + eje 002 (ecuación K0+171,358 = K0+170,980).

ESCALA 1:1000

0 10 20 30 40 50 m

PLANTA REALISTA

DISEÑO GEOMÉTRICO V2

PROYECTO

Vía Belén – Las Delicias
Cúcuta, Norte de Santander

CONTENIDO

Planta realista – tramo K1+380 – K1+609
TSD 6,00 m / 5,00 m – tramo final

SISTEMA

MAGNA-SIRGAS Origen Nacional
(CTM-12) · cotas en metros

ESCALA	LÁMINA
1:1000 · doble carta	**7 / 7**